


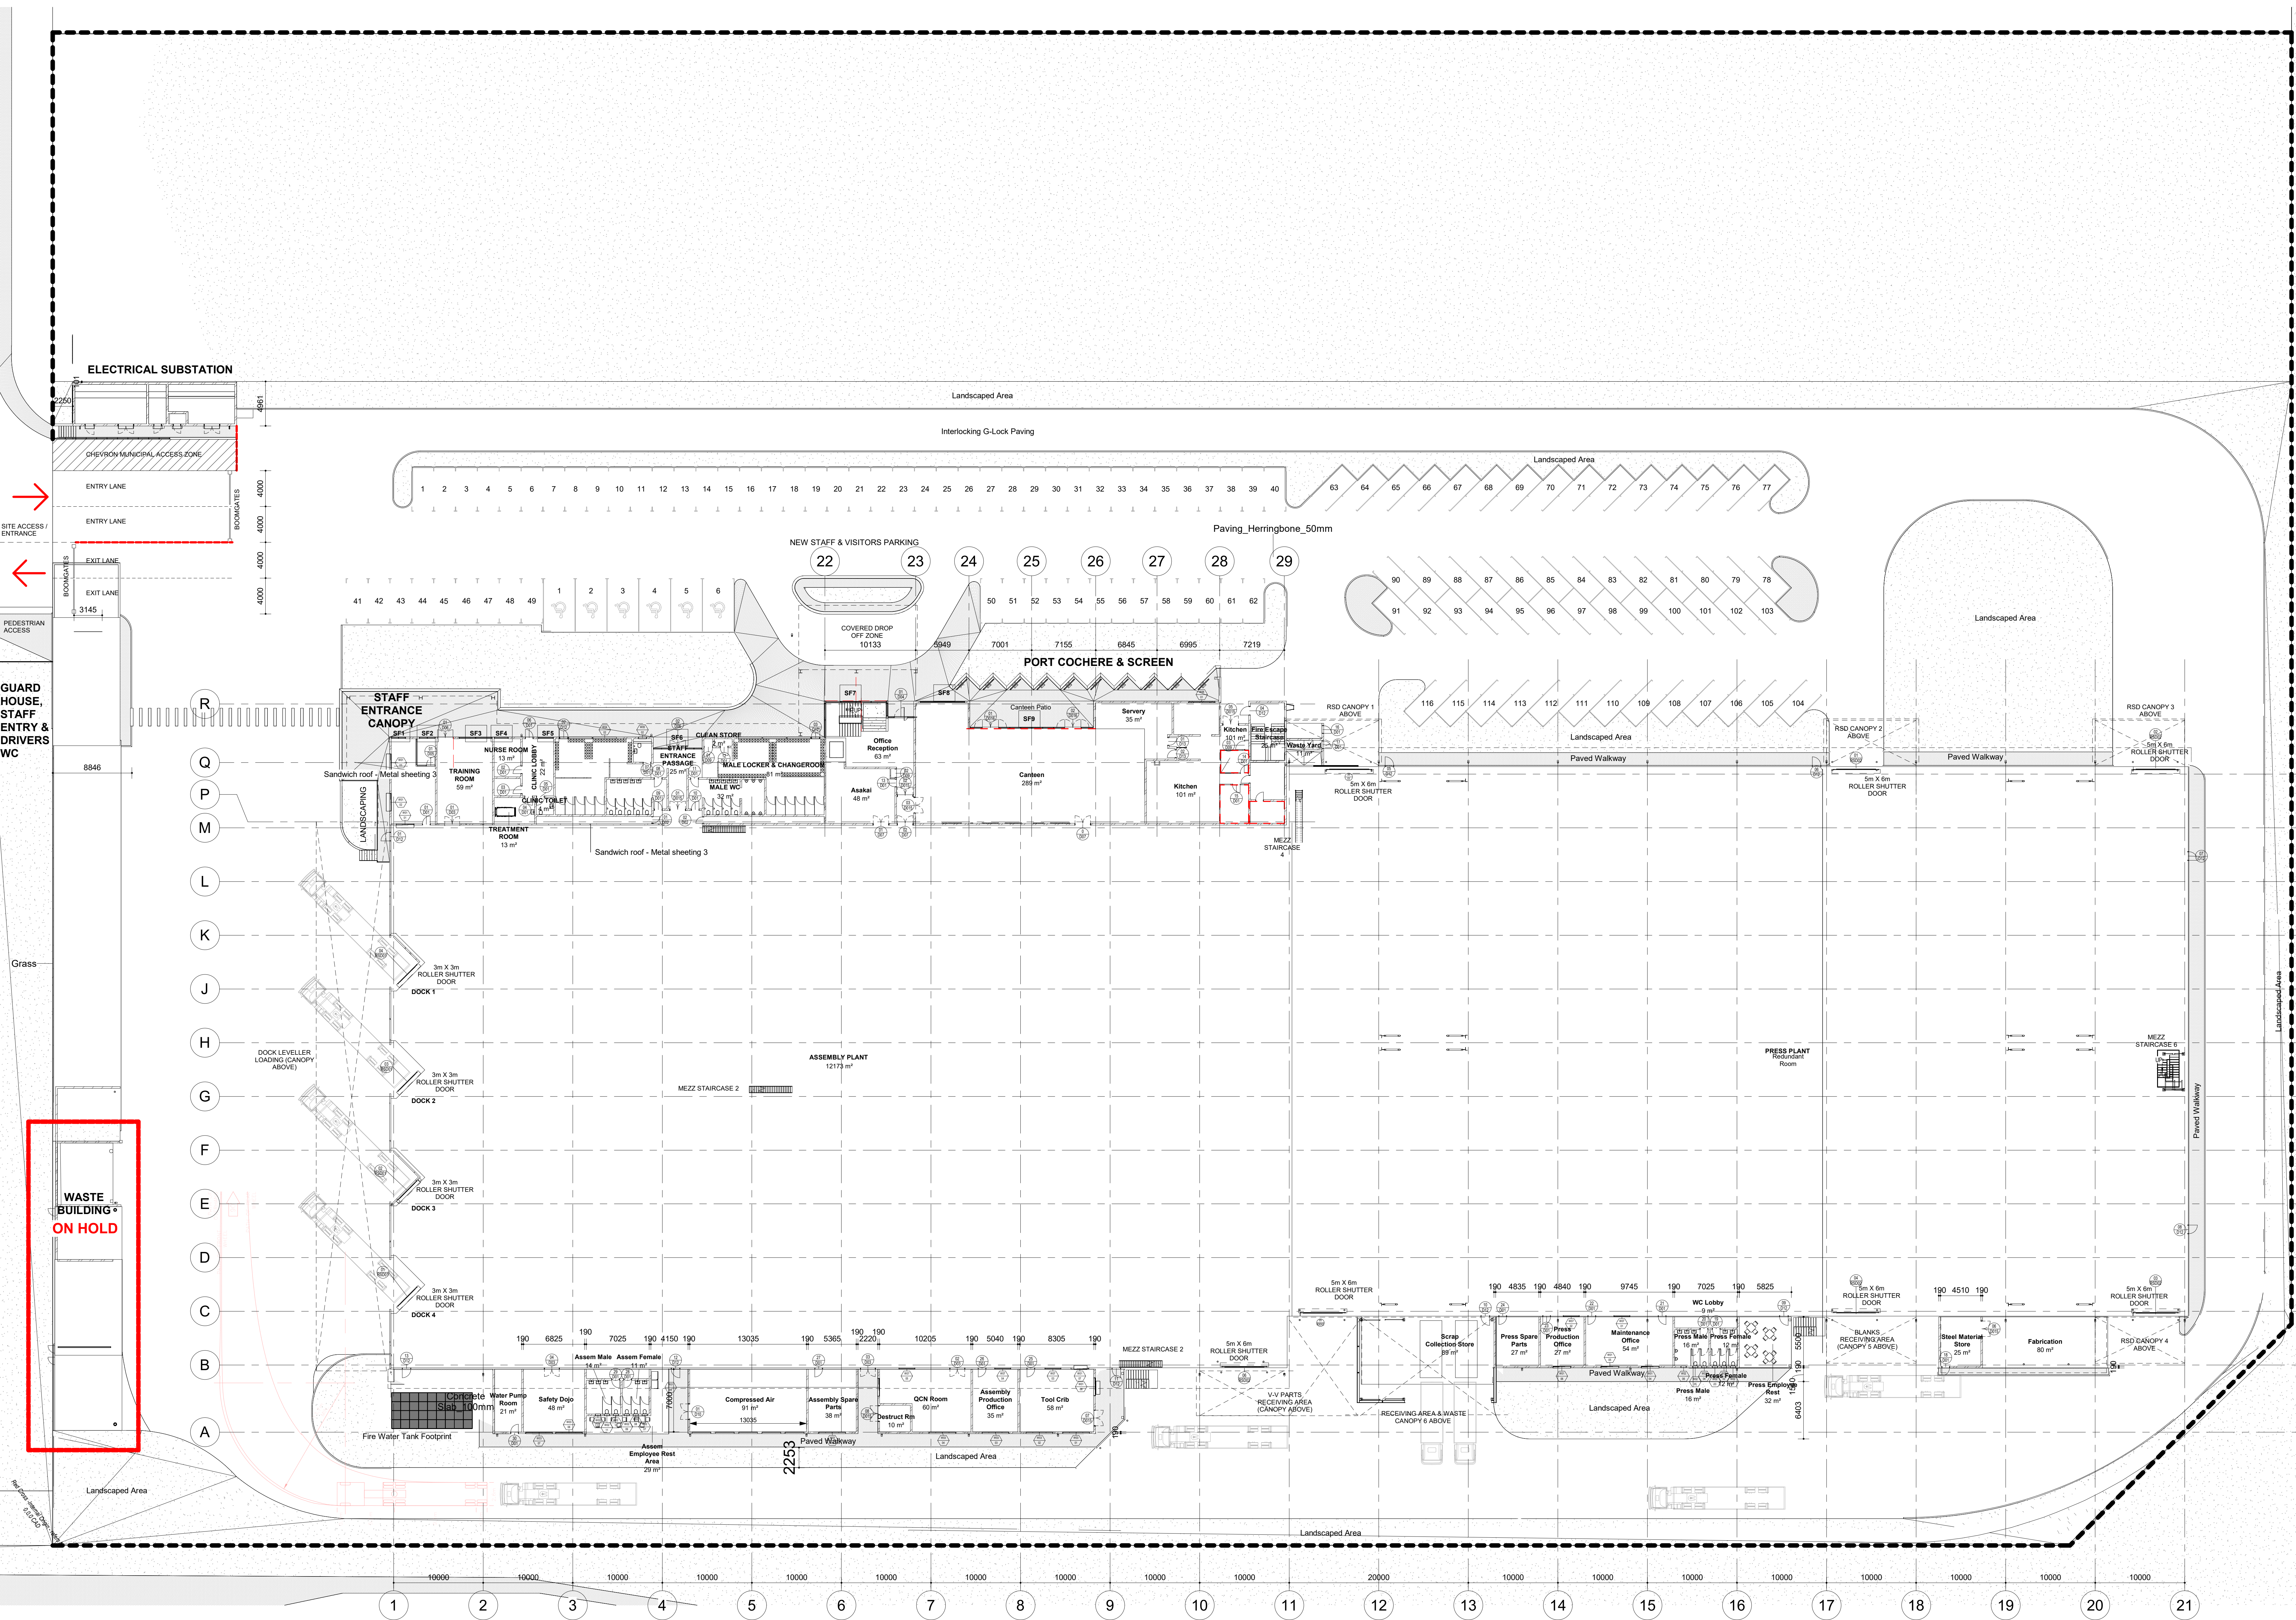

GUARD HOUSE, STAFF ENTRY & DRIVERS WC

WASTE BUILDING ON HOLD

000 GROUND FLOOR SCALE 1 : 250

- NOTES
1. ALL LEVELS AND DIMENSIONS ARE TO BE CHECKED ON SITE PRIOR TO COMMENCING ANY WORK. DISCREPANCIES ARE TO BE VERIFIED WITH THE ARCHITECT IMMEDIATELY. PRIOR TO THE COMMENCEMENT OF ANY WORK.
 2. ALL WRITTEN DIMENSIONS TO TAKE PREFERENCE OVER SCALED DIMENSIONS.
 3. ALL WORK TO BE IN ACCORDANCE WITH THE NATIONAL BUILDING REGULATIONS AND RELEVANT LOCAL AUTHORITY BY-LAWS.
 4. COPYRIGHT, PATENTS AND ALL INDUSTRIAL RIGHTS RESERVED.

REV	DESCRIPTION	DATE
00	Issued for Construction	2024.06.10
01	Revised revised layout	2024.06.10

NOTE: NO SILICONE PRODUCTS ALLOWED ON SITE

DESIGN CONSULTANT
STRUXIT PROJECTS

STRUXIT PROJECTS
21 Macos Blvd, Withead, uMhlanga, Durban, 4220
www.struxit.com

ARCHITECT
blue PROJECTS

BLUE PROJECTS INDUSTRIES (PTY) LTD
21 Macos Blvd, Withead, uMhlanga, Durban, 4220
www.blueprojects.com

OWNER
OGHARA SOUTH AFRICA PTY LTD / TOYOTA TSUSHO AFRICA
Ogihara (THAILAND) CO., LTD. **TOYOTA TSUSHO**

PROJECT TITLE
OGHARA PRESS PLANT DURBAN
31 HLAWE CLOSE, DUBE TRADEPORT PRECINCT, TRADEZONE 2, LA MERCY, KWAZULU-NATAL, SOUTH AFRICA
ERF 773 LA MERCY

DRAWING TITLE
GROUND FLOOR PLAN

APPROVED BY
MELISSA TRUSCOTT
ZAMASOM MZONELI

SCALE
1 : 250

DATE
06/08/2024

DRAWING INFORMATION
ZA019 BP 00 XX DR AR 010001 C 01