


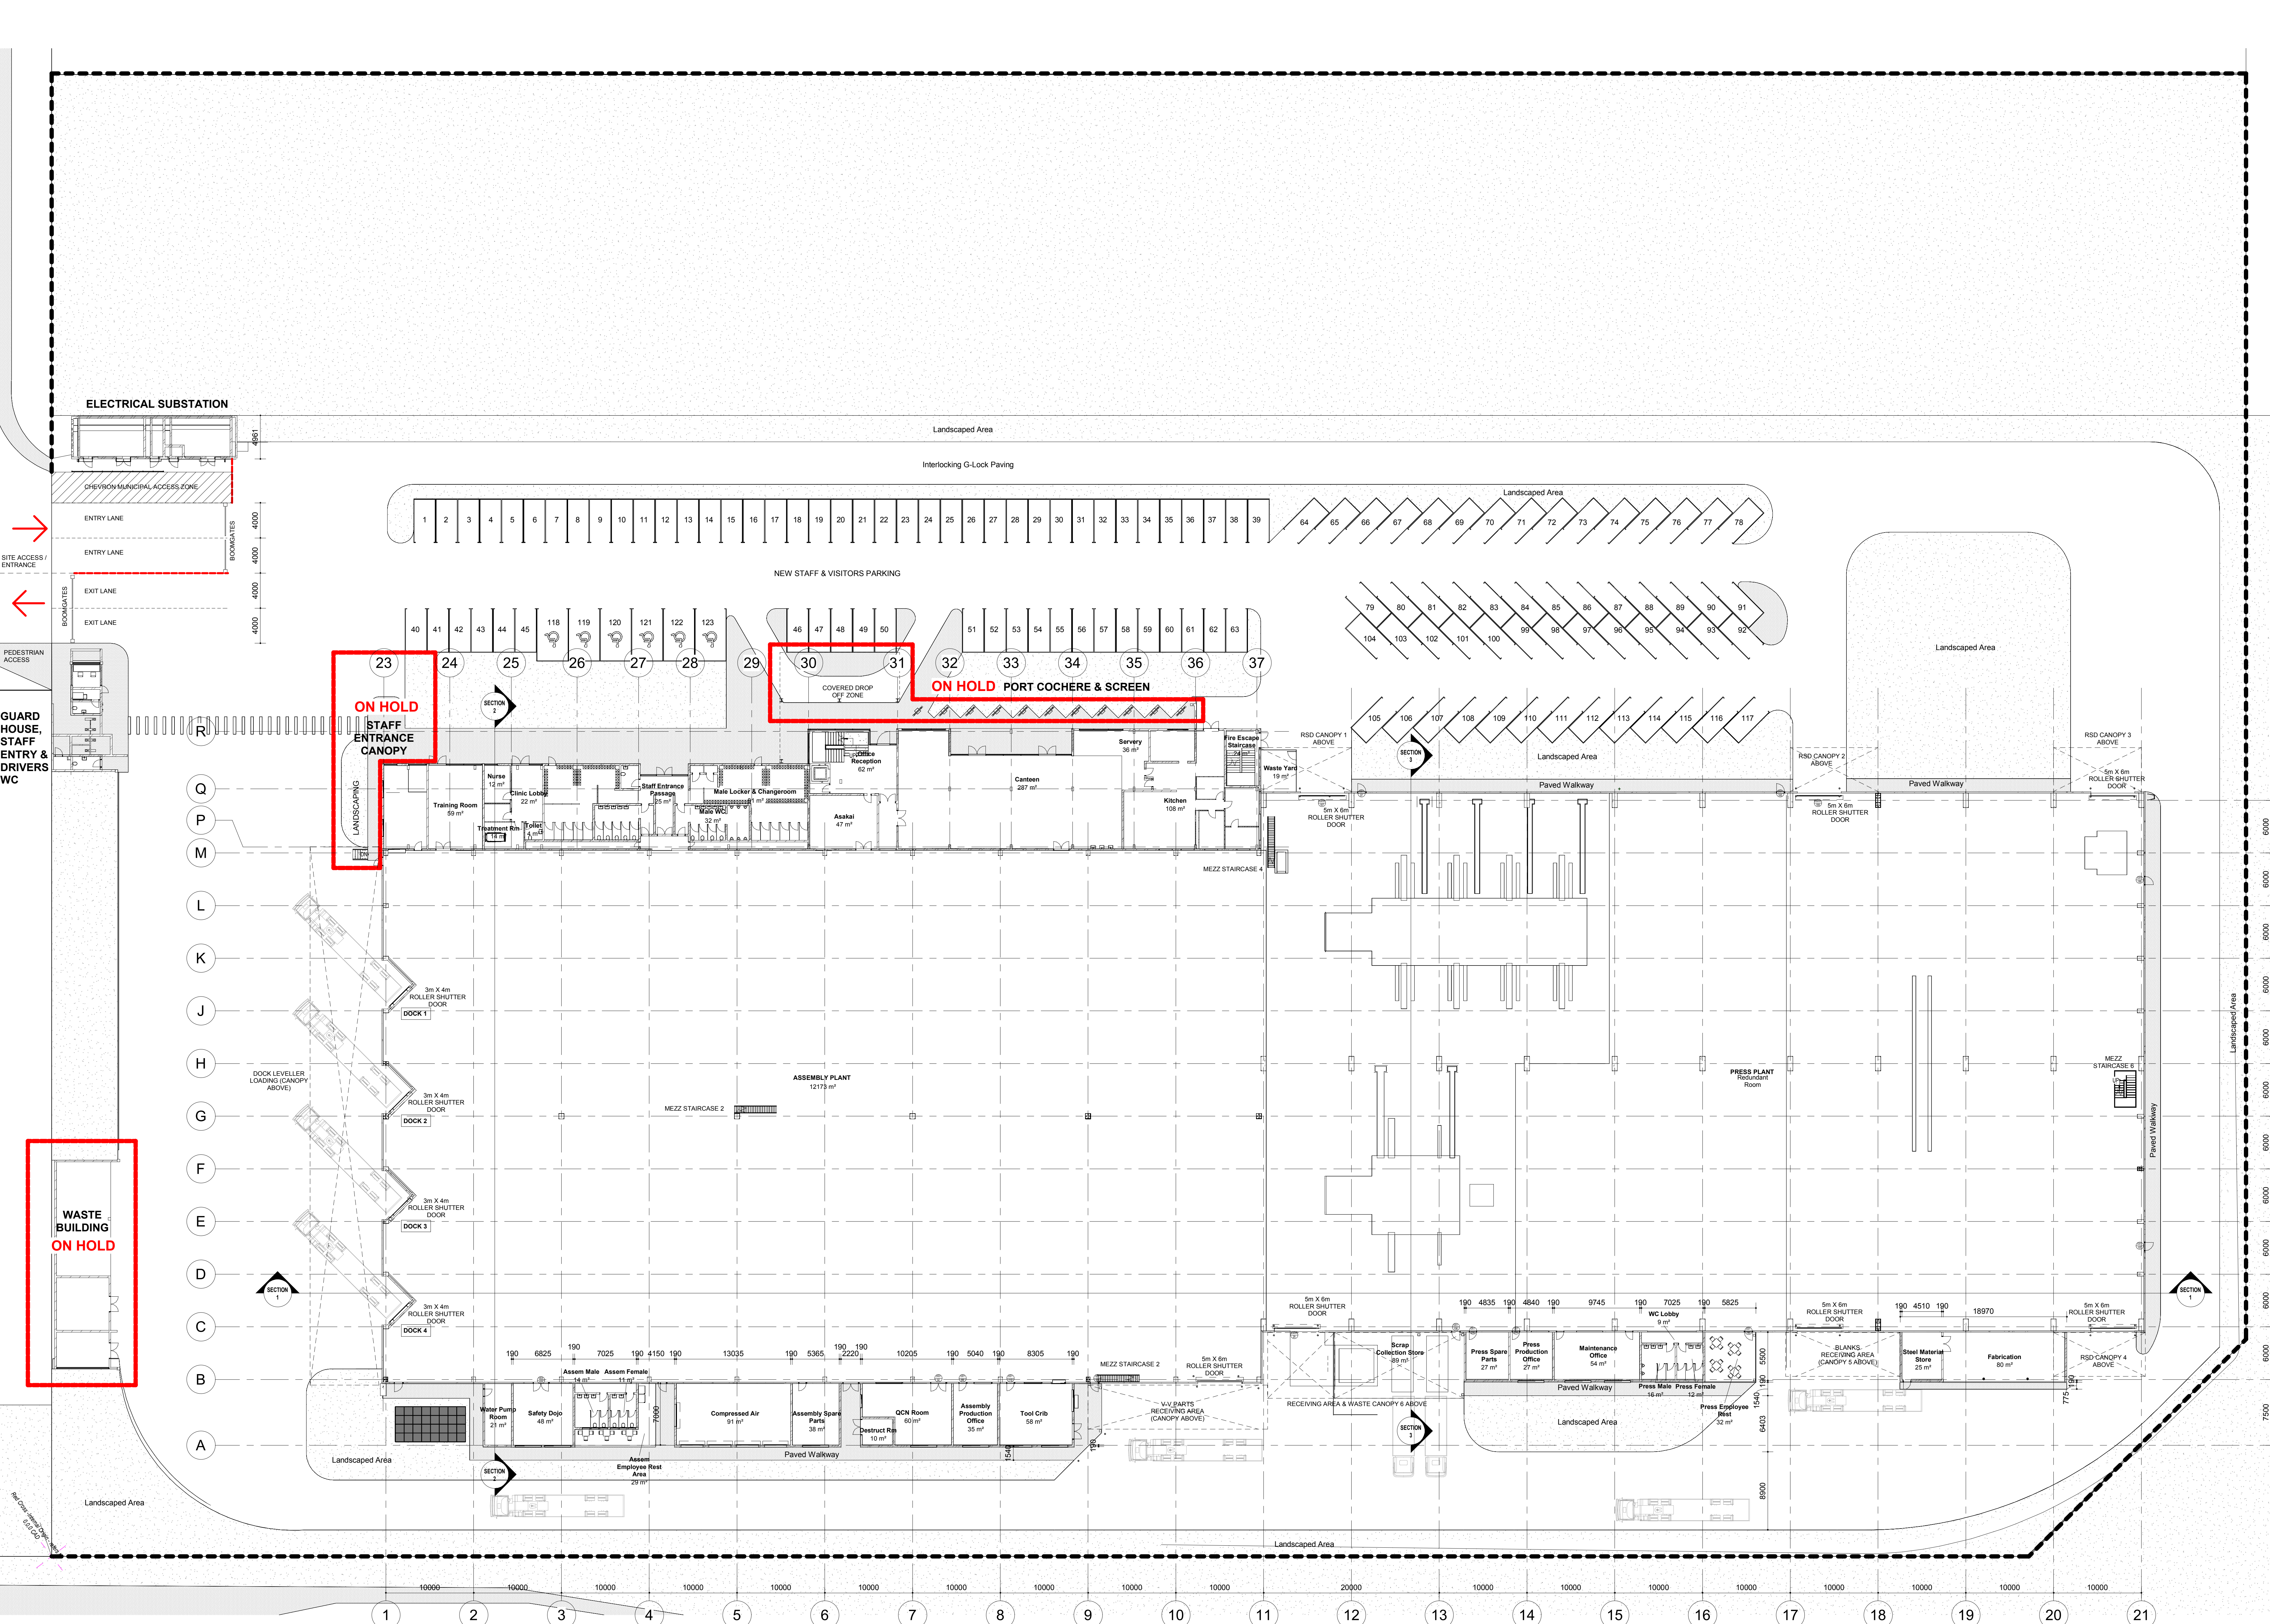

000_GROUND FLOOR
SCALE 1 : 250

NOTES		
1.	ALL LEVELS AND DIMENSIONS ARE TO BE CHECKED ON SITE PRIOR TO COMMENCING ANY WORK. DISCREPANCIES ARE TO BE VERIFIED WITH THE ARCHITECT IMMEDIATELY, PRIOR TO THE COMMENCEMENT OF ANY WORK.	
2.	ALL WRITTEN DIMENSIONS TO TAKE PREFERENCE OVER SCALED DIMENSIONS.	
3.	ALL WORK TO BE IN ACCORDANCE WITH THE NATIONAL BUILDING REGULATIONS AND RELEVANT LOCAL AUTHORITY BY-LAWS.	
4.	COPYRIGHT, PATENTS AND ALL INDUSTRIAL RIGHTS RESERVED.	
REVISIONS		
REV	DESCRIPTION	DATE
01	Issued for Construction	2024/06/10

KEYPLAN

DESIGN CONSULTANT

STRUXIT PROJECTS

STRUXIT PROJECTS
2 Neneza Blvd, Hillside, uMhlanga, Durban, 4300
www.struxit.com

CLIENT

blue PROJECTS

BLUE PROJECTS INDUSTRIES (PTY) LTD
21 Richmond Circle, Ridgeville, Durban, South Africa
www.blueprojects.com

OWNER

OGHARA SOUTH AFRICA PTY LTD / TOYOTA TSUSHO AFRICA

Ogihara
(THAILAND) CO., LTD.

TOYOTA TSUSHO

PROJECT TITLE

OGHARA PRESS PLANT DURBAN
31 HLAWE CLOSE, DUBE TRADEPORT PRECINCT, TRADEZONE 2, LA MERCY, KAWULU NATAL, SOUTH AFRICA
ERF 773 LA MERCY

DRAWING TITLE

GROUND FLOOR PLAN

APPROVED BY

MELISSA TRUSCOTT

DRAWN BY

MARSHNEE WOODLIAR

SCALE

1 : 250

DATE

10/06/2024

DRAWING INFORMATION

ZA019 BP 00 XX DR AR 010001 C 00